


PLANO DE DISPOSICIÓN — AGRIVOLTAICO URABÁ (Apartadó, Antioquia) · Terreno 32 × 100 m

3.200 m² · Ocupación FV ~30% (950 m²) · 17 matrices de 2×9 = 306 paneles JA Solar JAM66D46-720/LB bifacial · 220,3 kWp · ALTURA LIBRE 3,0 m

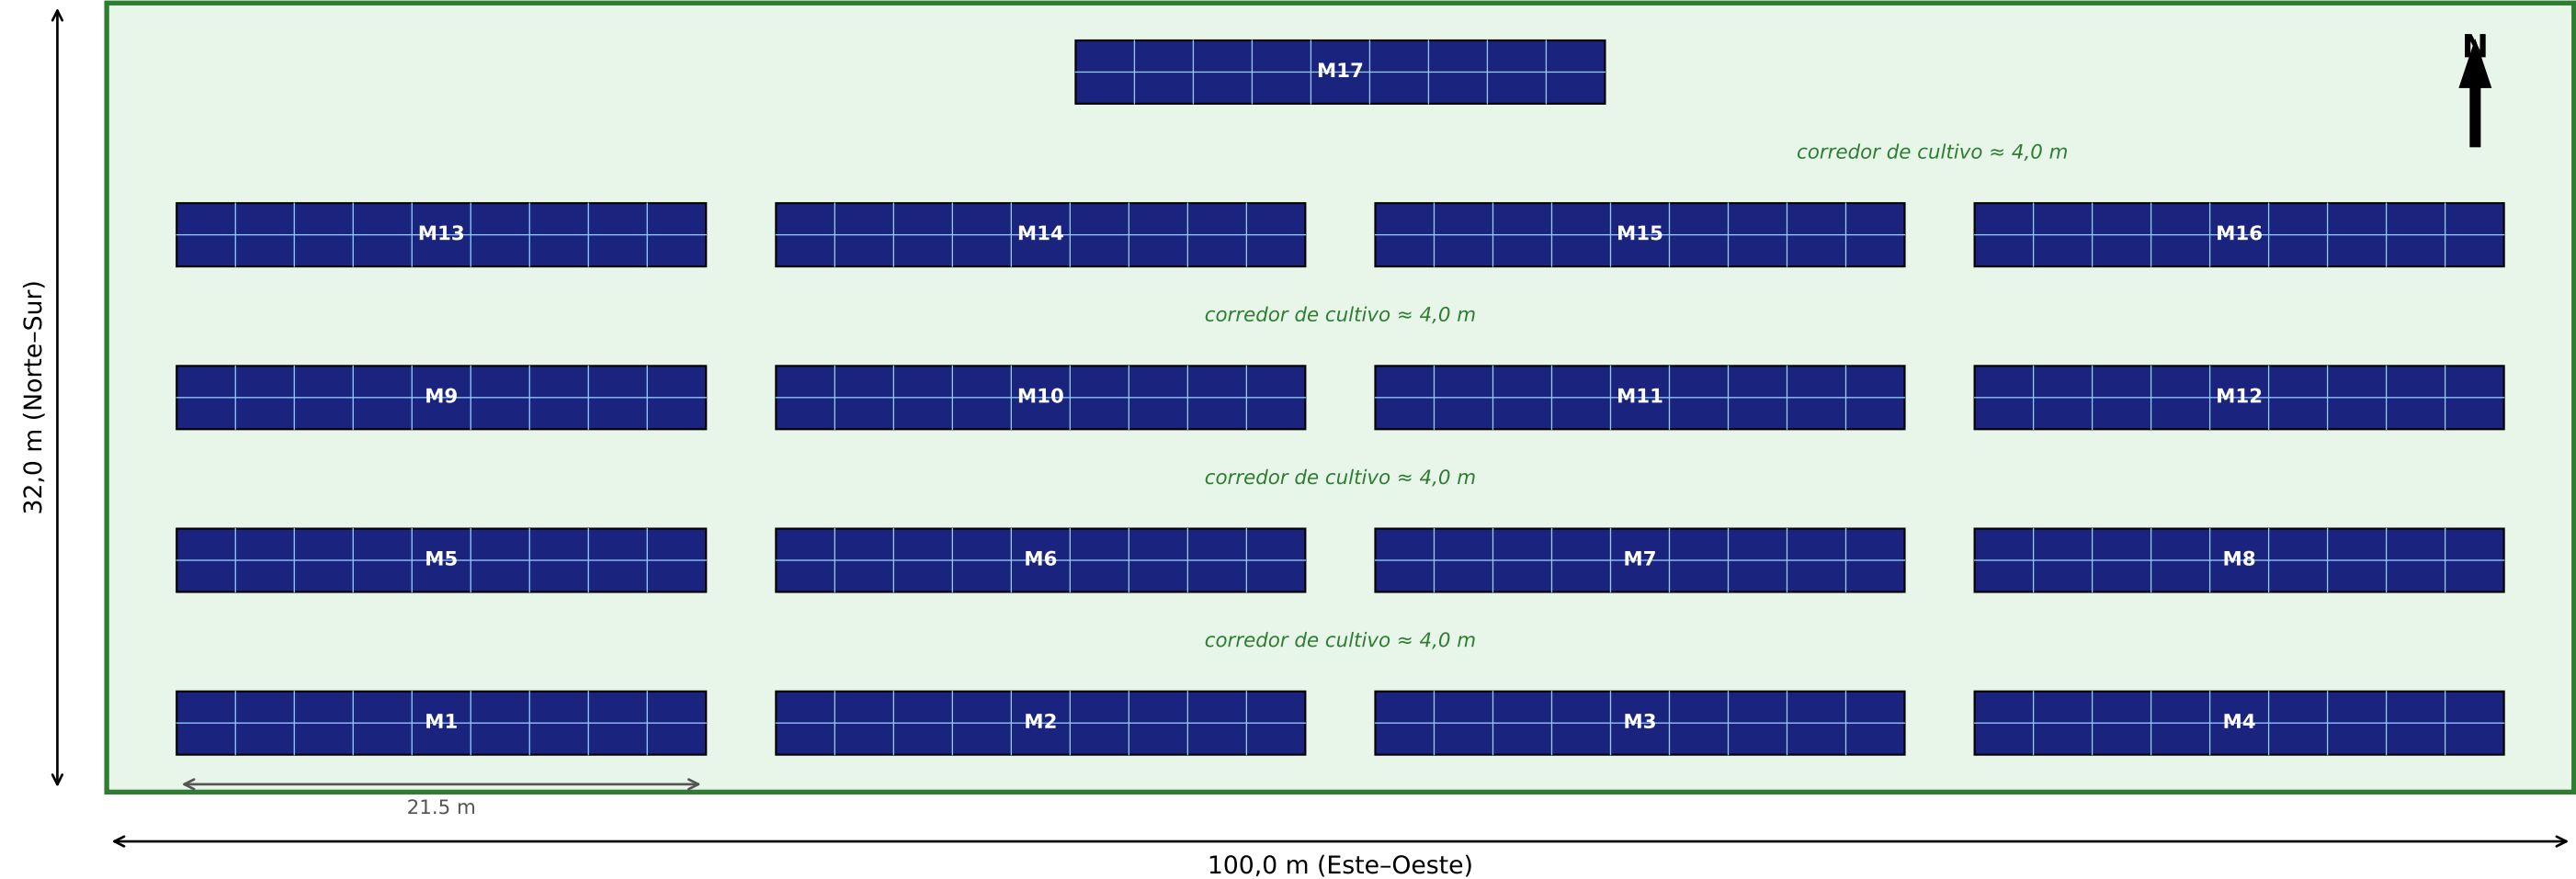

Supuesto: el lado de 100 m corre Este-Oeste (filas mirando al Sur). Si corre Norte-Sur, se gira la disposición.
Matriz: 2 filas x 9 paneles apaisados = 18 paneles · huella 21,5 x 2,6 m · inclinación 10° al Sur
ALTURA LIBRE AL SUELO: 3,0 m (borde inferior del panel) — cultivo y maquinaria bajo los paneles
4 corredores de cultivo de ≈4,0 m + pasillos de 2,8 m entre matrices · tornillo de tierra · estructura ZAM