


PLANO DE DISPOSICIÓN — AGRIVOLTAICO URABÁ (Apartadó, Antioquia) · Terreno 32 × 100 m

3.200 m² · Ocupación FV ~30% (950 m²) · 17 matrices de 2×9 = 306 paneles JA Solar JAM66D46-720/LB bifacial · 220,3 kWp

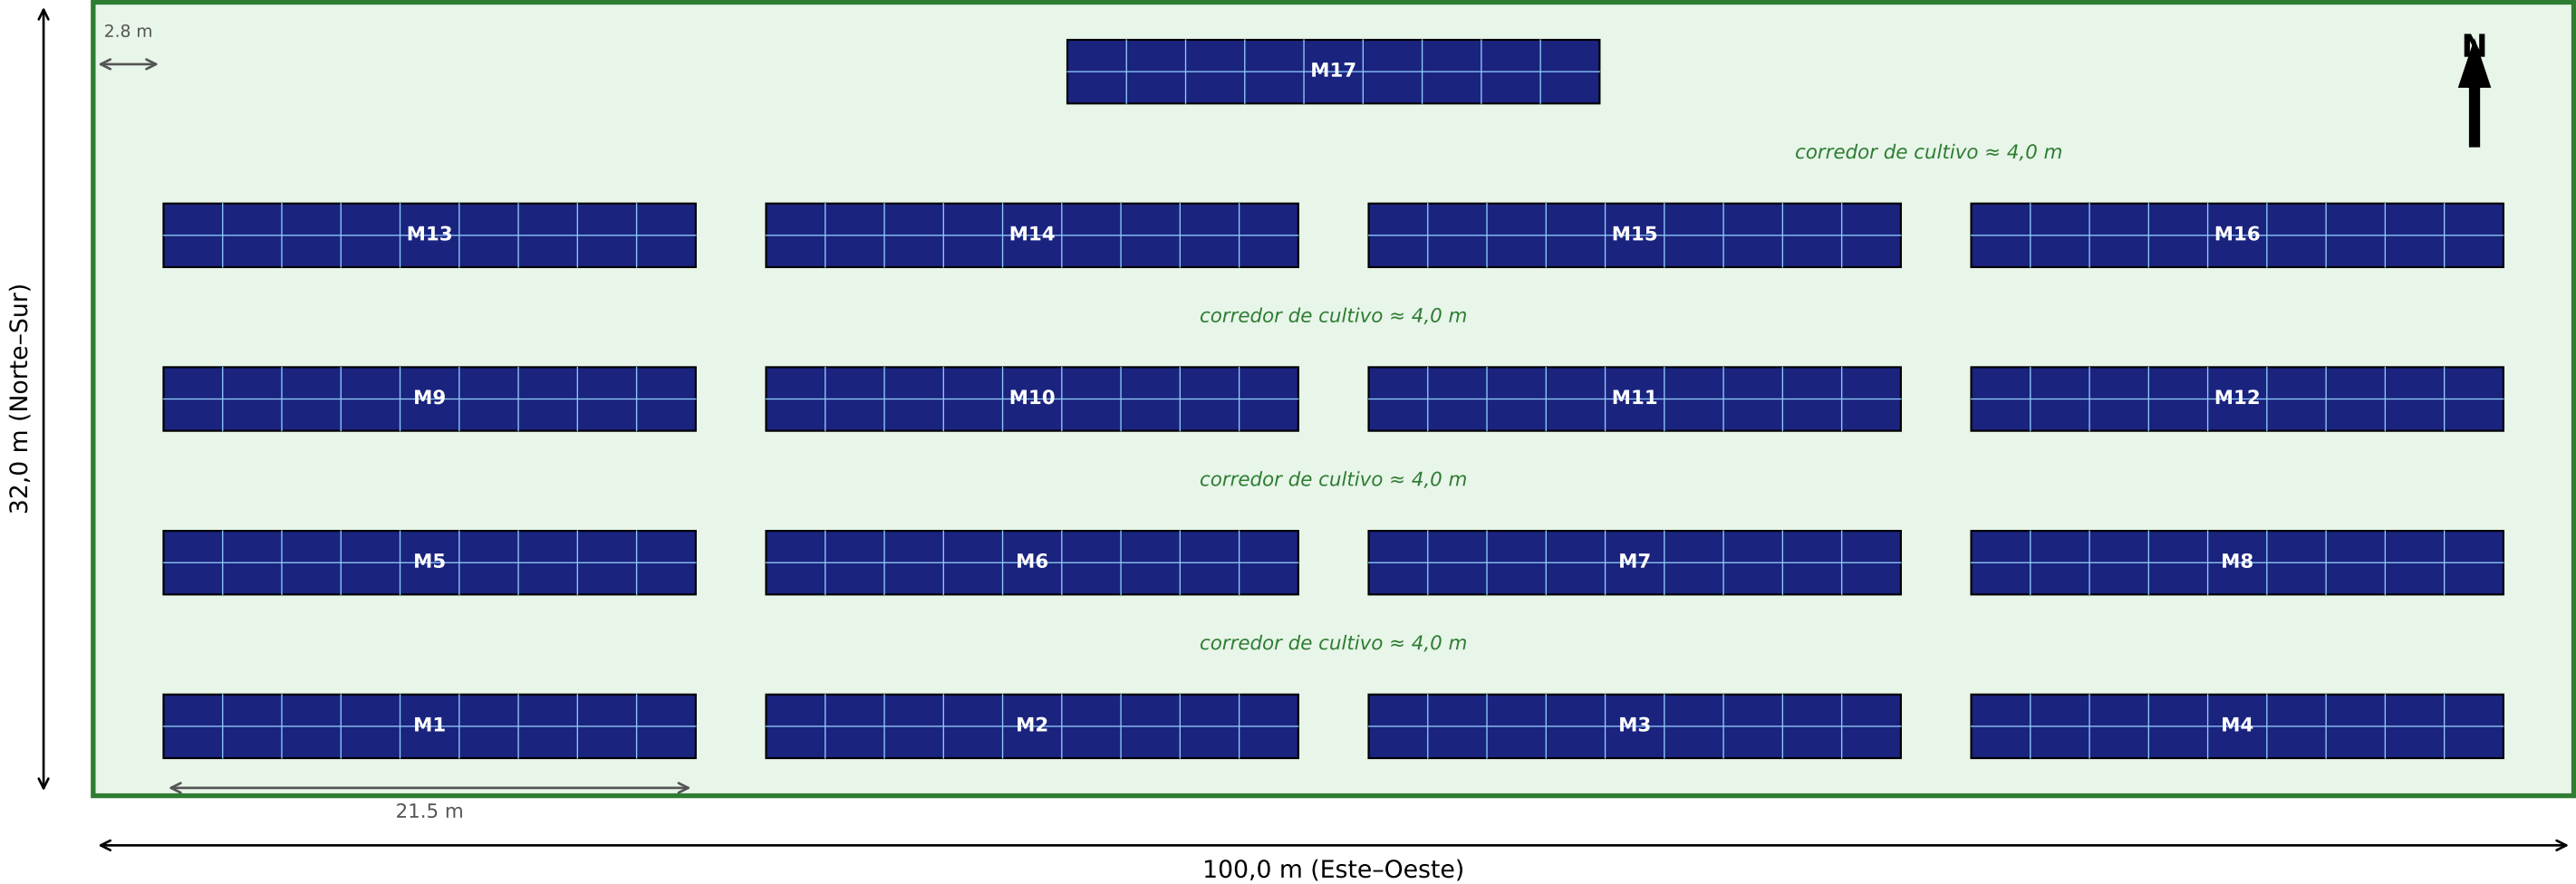

Supuesto: el lado de 100 m corre Este-Oeste (filas mirando al Sur). Si el lado largo corre Norte-Sur, avísame y giro la disposición.
Matriz: 2 filas × 9 paneles apaisados = 18 paneles · huella 21,5 × 2,6 m · inclinación 10° al Sur · altura libre 2,5 m
4 corredores de cultivo de $\approx 4,0$ m entre filas + pasillos de 2,8 m entre matrices · cimentación tornillo de tierra · estructura ZAM