


PLANO DE DISPOSICIÓN — AGRIVOLTAICO URABÁ (Apartadó, Antioquia)

Terreno 3.200 m² (80×40 m) · Ocupación FV 30% · 17 matrices de 2×9 = 306 paneles JA Solar JAM66D46-720/LB bifacial · 220,3 kWp

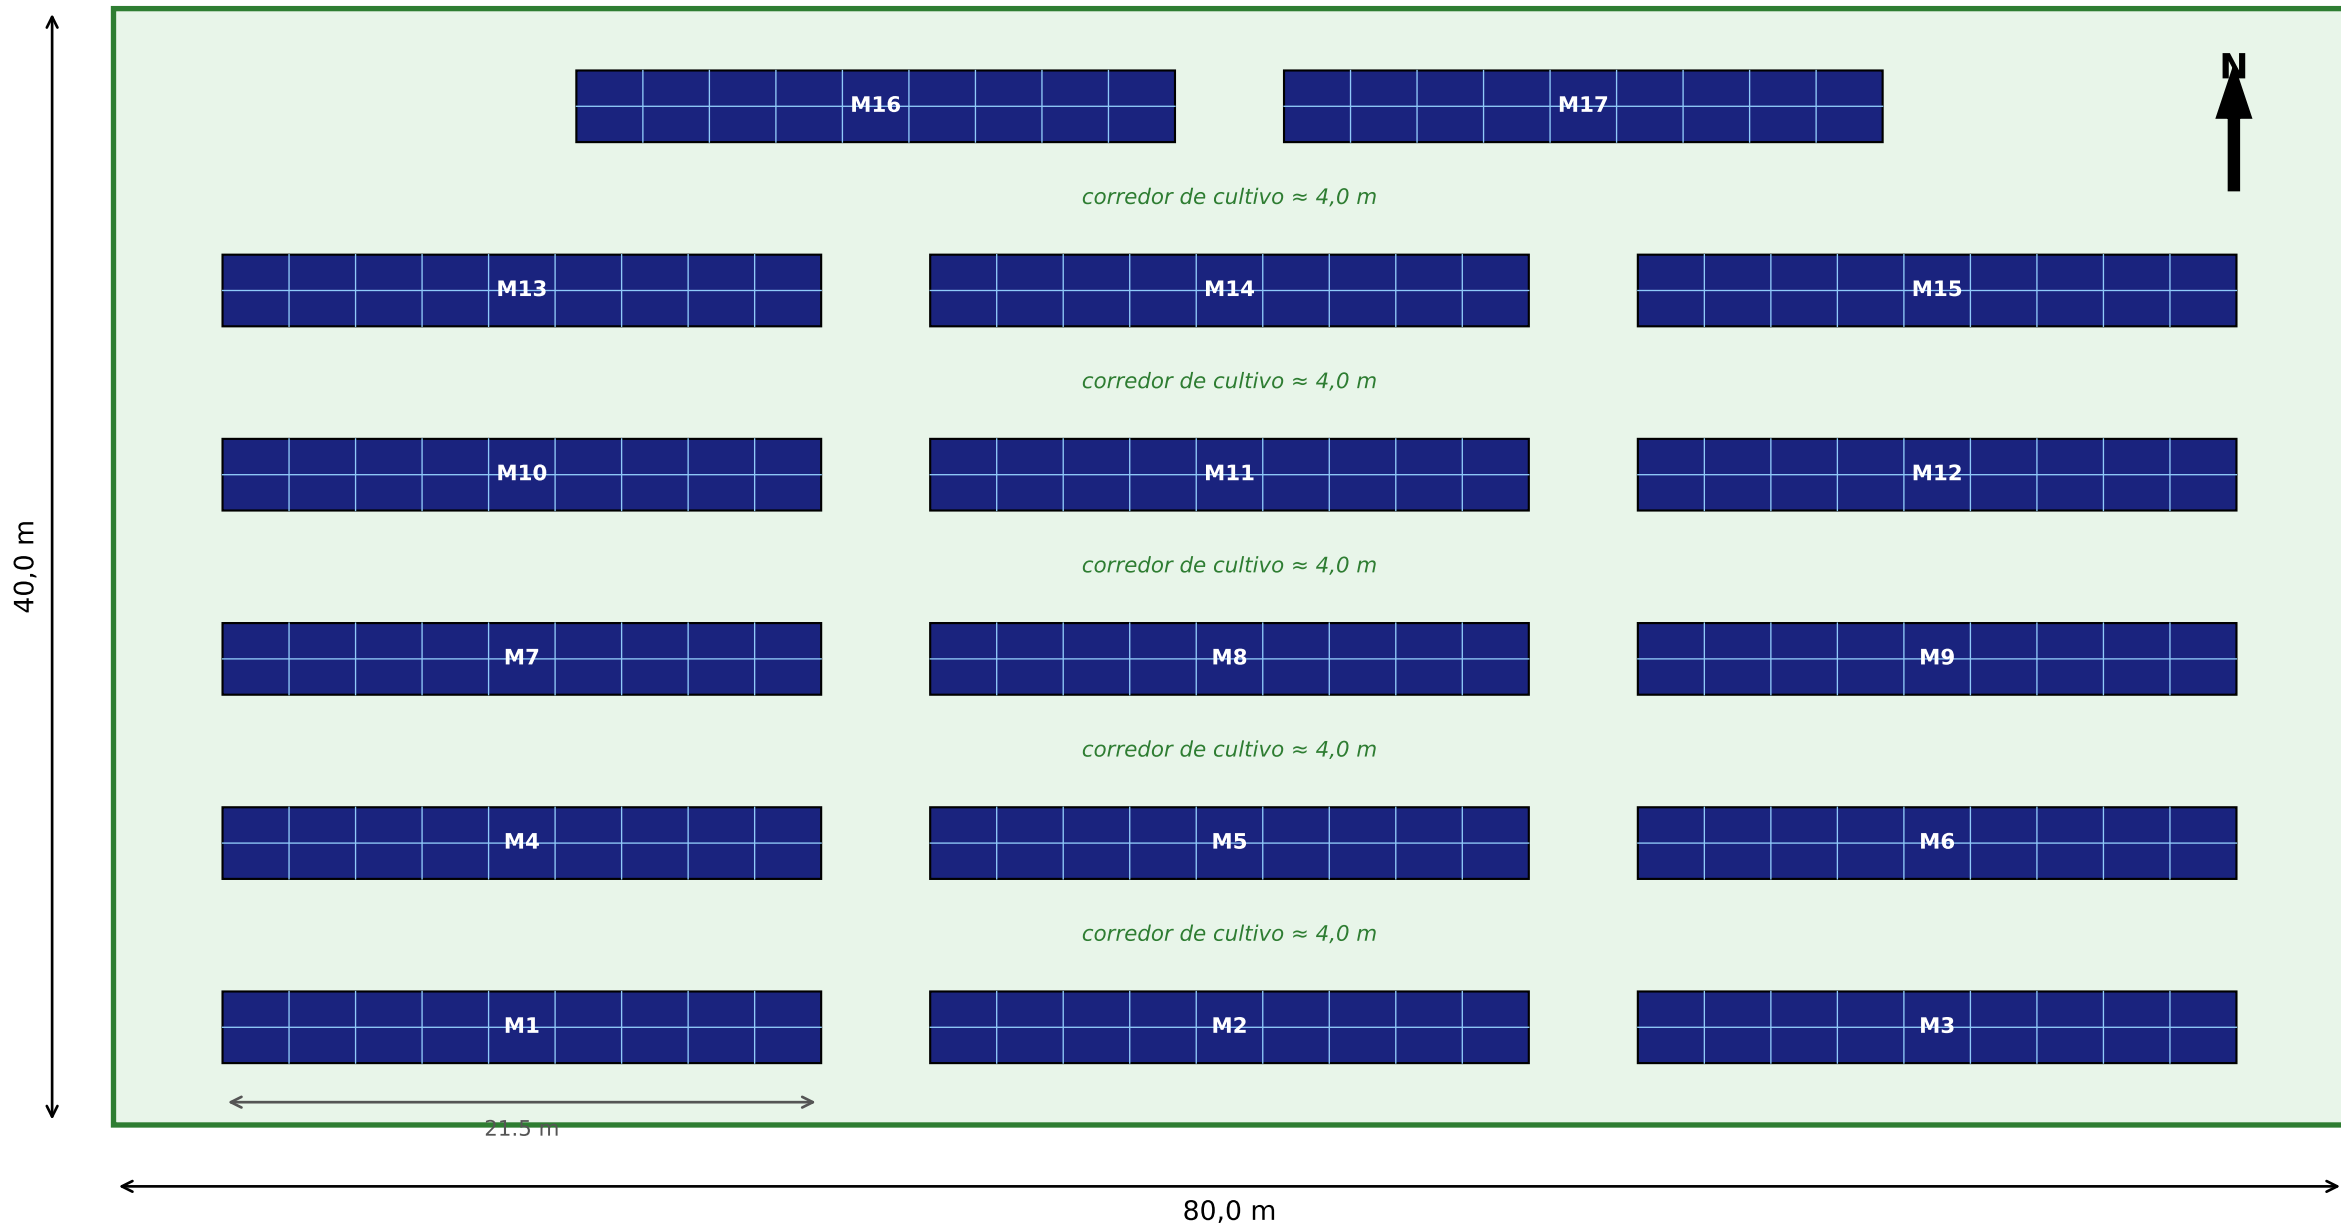

Matriz: 2 filas × 9 columnas (apaisado) = 18 paneles · huella 21,5 × 2,6 m
Inclinación 10° orientada al SUR · altura libre al suelo 2,5 m (cultivo/maquinaria)
Cimentación: tornillo de tierra · estructura ZAM (Magnesil)
Filas orientadas Este-Oeste · paneles miran al Sur · lat 7,884° / lon -76,635°